

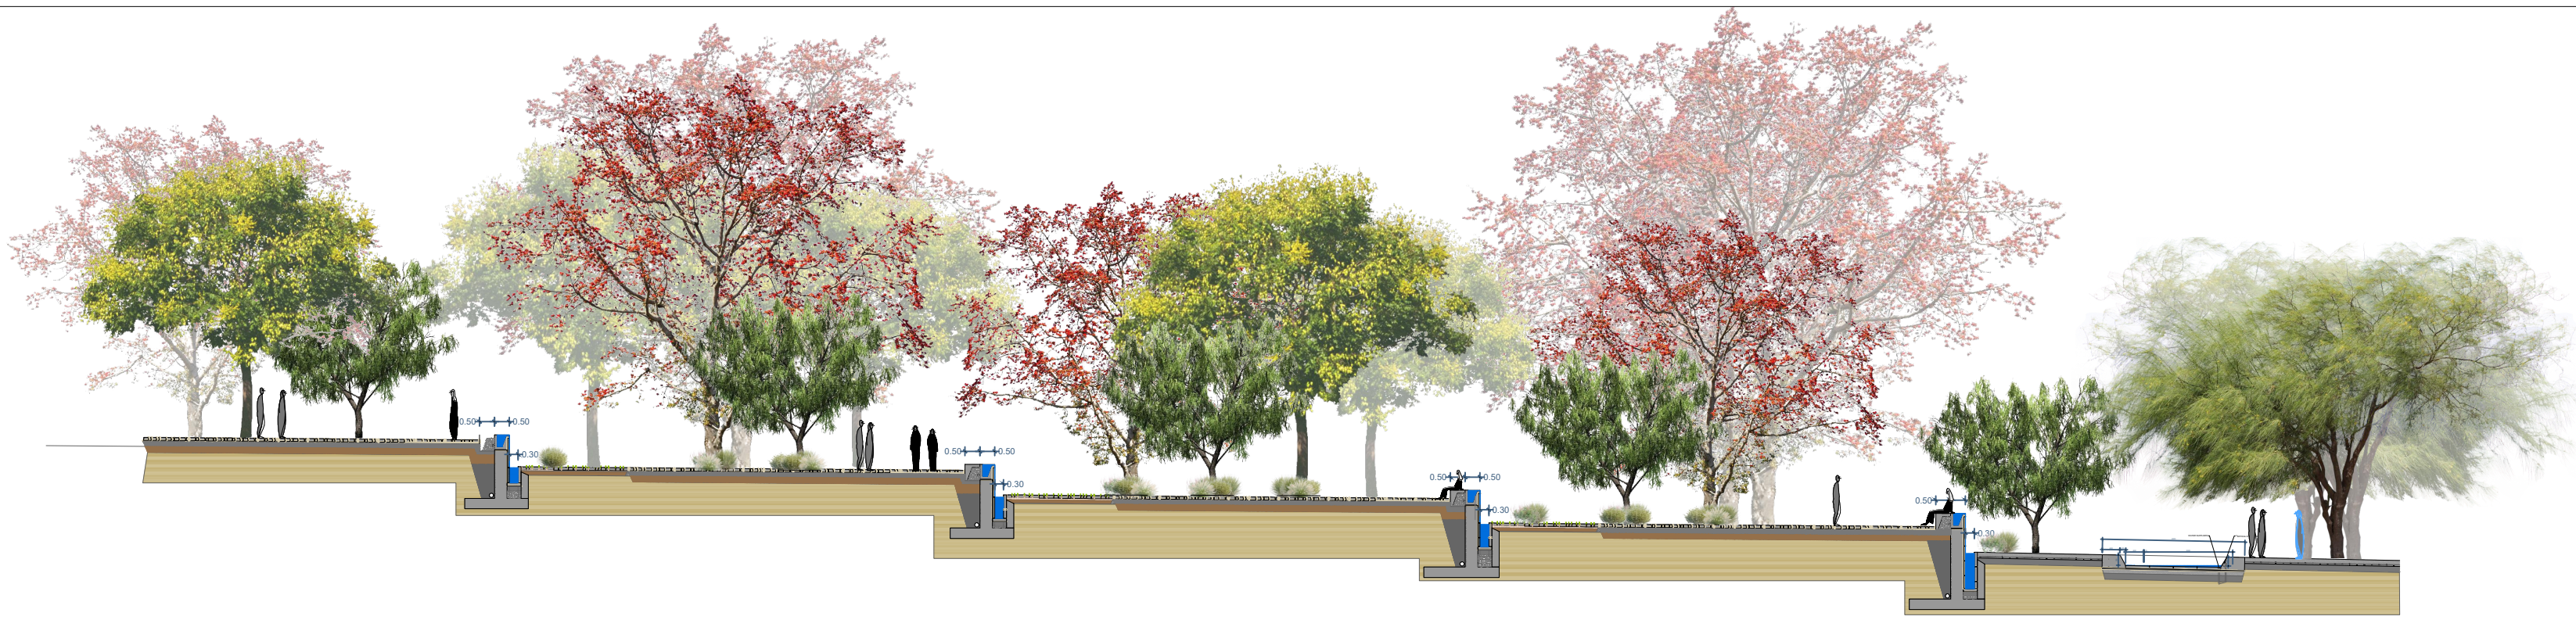


100
0 10
Millimetres

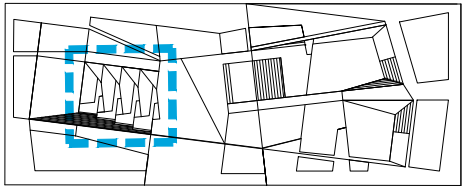

SECTION

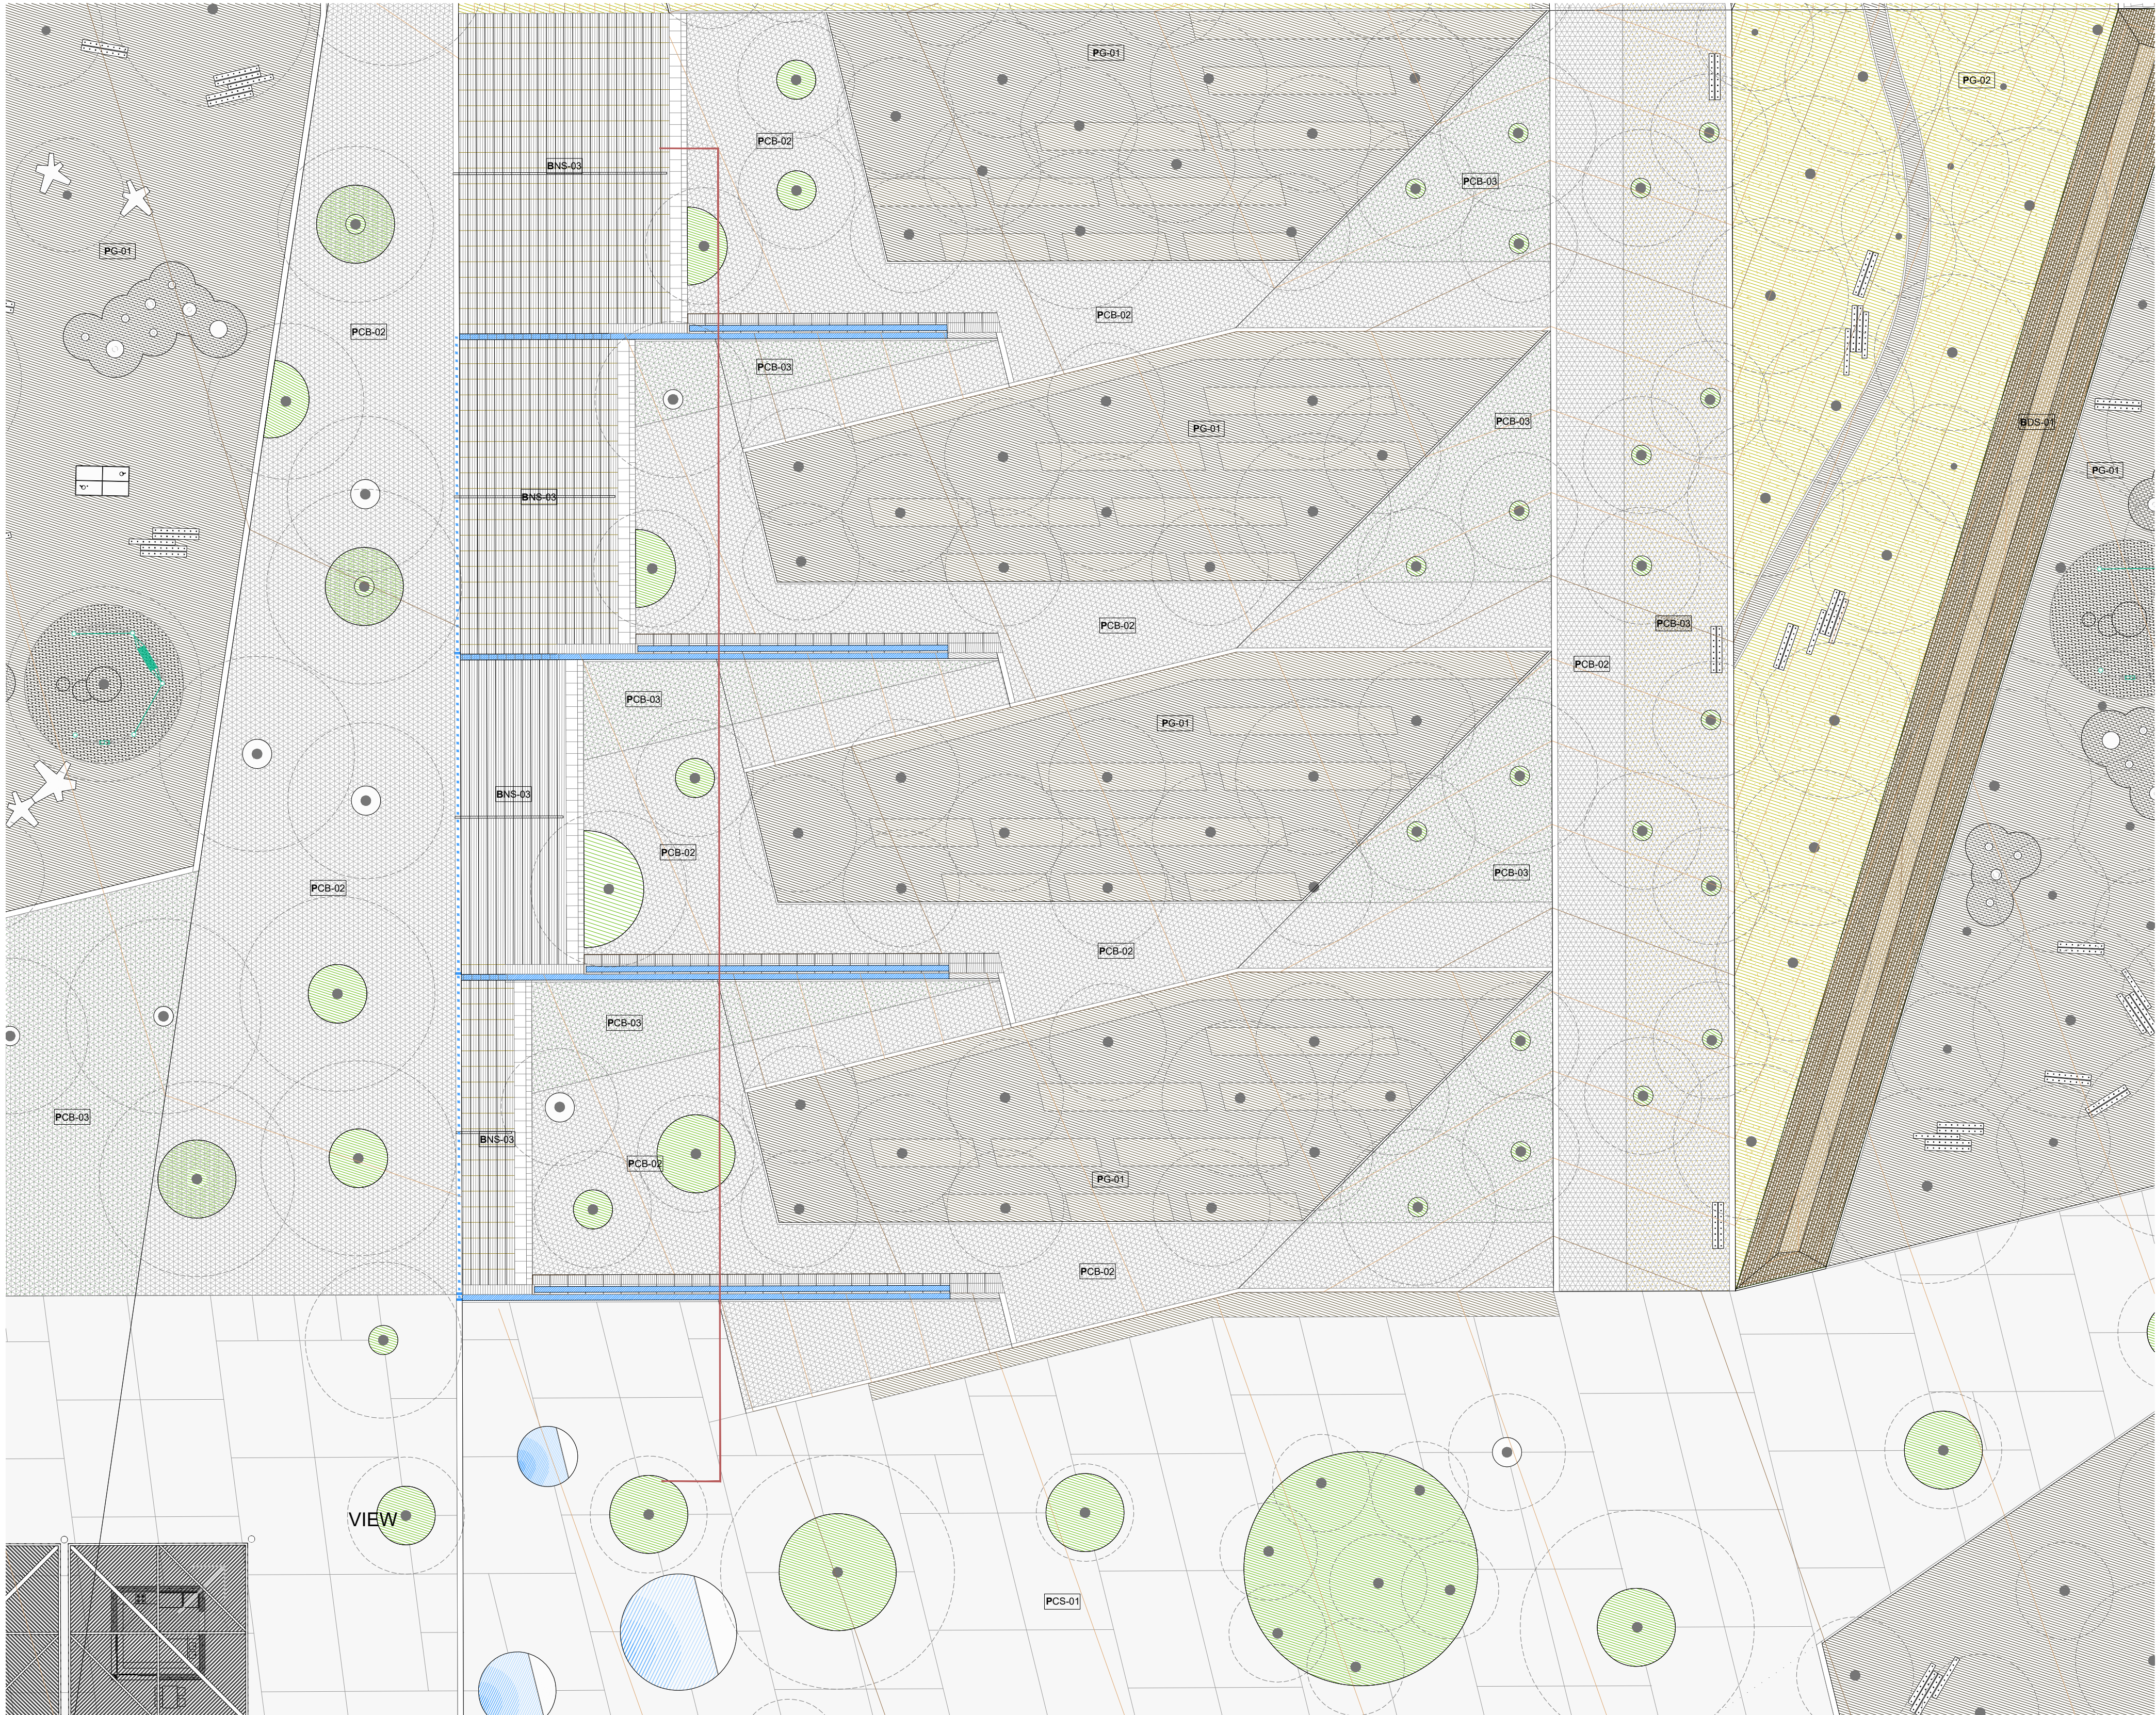

PAVEMENT LEGEND

PG-01	Compacted Ground
PG-02	Precast Concrete Blocks Irregular Shape 21x13x10cm
PG-03	Precast Concrete Blocks, Open Joint Irregular Shape 21x13x10cm
PG-04	Concrete Slab (Type 1)
PG-05	Sealed Gravel
PG-06	Filter Mat Substrate (60% sand, 20% topsoil, 20% compost)
BNS-01	Natural Stone Bleachers - Riyadh Sandstone (50x80x15cm)

For more information on WATER SUPPLIERS & DRAINAGE please refer to the drawings
JVEA-GRP-MON-WTF-MEP

GENERAL CONSTRUCTION NOTES

- ALL LEVELS & DIMENSIONS SHOWN ON THIS DRAWING ARE INDICATED IN METERS
- THIS DRAWING IS INDICATIVE OF ARCHITECTURAL REQUIREMENTS ONLY. THIS DRAWING SHALL BE READ IN CONJUNCTION WITH ALL RELATED ARCHITECTURAL, STRUCTURAL, CIVIL AND SERVICES DRAWINGS. ANY DISCREPANCIES BETWEEN ARCHITECTS AND ENGINEERS DRAWINGS ARE TO BE REPORTED TO THE LANDSCAPE ARCHITECT.
- THE CONTRACTOR IS RESPONSIBLE FOR COORDINATION OF ENGINEERS REQUIREMENTS. THESE INCLUDE, BUT ARE NOT LIMITED TO, STRUCTURAL, MECHANICAL, CIVIL, ELECTRICAL, REQUIREMENTS (REFERS TO TYPICAL ITEMS SUCH AS FOOTINGS, MATERIALS, MATERIAL THICKNESS, STABILIZATION, RETENTION, IRRIGATION, WATER SUPPLY, WATER FEATURES, STORM WATER, ELECTRICAL, ETC.) ITEMS APPROVED BY AN ENGINEER REQUIRES COORDINATION WITH SUPERVISING LANDSCAPE ARCHITECT PRIOR TO CONSTRUCTION OR MANUFACTURE.
- THE DESIGN INDICATES TYPICAL ARCHITECTURAL REQUIREMENTS TO SHOW THE DESIGN INTENT FOR THE DEVELOPMENT OF SHOP DRAWINGS. IT IS THE RESPONSIBILITY OF THE CONTRACTOR TO SUPPLY A COMPLETE SOLUTION WHEN DEVELOPING SHOP DRAWINGS OR CONSTRUCTION, WHICH IS NOT LIMITED TO TYPICAL ELEMENTS ONLY. FOR INSTANCE, INCLUDE END/CORNER PIECES OR SPECIAL ELEMENTS ACCORDING TO DESIGN REQUIREMENTS. DEVELOP ALL SUCH DETAILS IN COORDINATION WITH SUPERVISING ARCHITECT.
- ALL DIMENSIONS, LEVELS AND QUANTITIES SHOWN ON THIS DRAWING ARE INDICATIVE ONLY. BEFORE STARTING ANY SITE WORKS, ALL FINISHED FLOOR LEVELS AND DIMENSIONS HAVE TO BE CHECKED AND VERIFIED BY THE CONTRACTOR PRIOR TO CONSTRUCTION OR MANUFACTURE OF PRODUCTS. ANY DISCREPANCIES MUST BE REPORTED TO THE SUPERVISING LANDSCAPE ARCHITECT PRIOR TO CONSTRUCTION OR MANUFACTURING.
- THE INTERFACE BETWEEN MECHANICAL ITEMS, MATERIALS, ELEMENTS OR METHOD OF FIXATION, ARE TO BE DESIGNED, FINISHED IN AN AESTHETICALLY ACCEPTABLE MANNER. COORDINATE REQUIREMENTS WITH SUPERVISING LANDSCAPE ARCHITECT.
- LANDSCAPE RELATED MATERIALS INDICATED OR REQUIRED ARE SUBJECT TO BE SUBMITTED AS MOCK-UPS FIRST TO DETERMINE FINISHES, QUALITY ETC. ONLY ONCE INDIVIDUAL WRITTEN APPROVAL IS OBTAINED, MAY ELEMENTS BE MANUFACTURED.
- THE REQUIREMENTS FOR MATERIALS USED FOR CONSTRUCTION IN EXTERIOR AREAS, SUCH AS ADHESION, COATINGS, SEALING, WATERPROOFING OR EXPANSION JOINTS ETC. SHOULD CARRY A MINIMUM WRITTEN GUARANTEE OF 10 YEARS BY SUPPLIER, UNLESS OTHERWISE AGREED WITH THE OWNER.
- CONSTRUCT ALL ELEMENTS ACCORDING TO ACCEPTABLE INTERNATIONAL NORMS OR SAFETY REQUIREMENTS. IT IS THE RESPONSIBILITY OF THE CONTRACTOR TO ENSURE REQUIREMENTS ARE MET. INCLUDE WARNING SIGNS WHERE APPLICABLE AND COORDINATE LOCATIONS WITH SUPERVISING LANDSCAPE ARCHITECT.
- ENSURE ALL ELEMENTS ARE CONSTRUCTED AND FULFILL TO ACCOMMODATE HANDICAP OR DISABLED ACCESS OR REQUIREMENTS WITH INTERNATIONAL NORMS AND STANDARDS.
- WHERE NO ARABIAN MUNICIPALITY OR SAUDI ARABIAN STANDARD IS AVAILABLE, CONSTRUCTION SHALL FOLLOW REQUIREMENTS OF THE HIGHEST INTERNATIONAL STANDARD I.E. AMERICAN OR EUROPEAN ETC.
- DISCREPANCIES BETWEEN DRAWN AND EXISTING SITE CONDITIONS TO BE ADJUSTED AND RESOLVED BY SUPERVISING LANDSCAPE ARCHITECT.

AF	SEP 2023	DETAILED DESIGN	XXX	XXX	XXX
AE	JUL 2023	DETAILED DESIGN	XXX	XXX	XXX
AD	APR 2023	DETAILED DESIGN	XXX	XXX	XXX
AC	MAR 2023	DETAILED DESIGN	XXX	XXX	XXX
AB	FEB 2023	DETAILED DESIGN	XXX	XXX	XXX
AA	DEC 2022	DETAILED DESIGN	XXX	XXX	XXX
Rev.	Date	Description	By	Chk'd	App'd

CLIENT	DESIGNER

Project Title
**LANDSCAPE DESIGN OF CITY PARKS, AR-RIMAL
2, AL-QADISIYAH 3, AL-MONASYA , TWAEQ 2**

Drawing Title
**AL-MONASYA
WATER FEATURES GENERAL PLAN**

Scale	Designed	Drawn	Checked	Approved
1:200	XXX	XXX	XXX	XXX
Original Size	Date	Date	Date	Date
A1	SEP 2023	SEP 2023	SEP 2023	SEP 2023
Drawing Number	JVEA-GRP-MON-WTF-5101			Revision
				AF

0 2 4 10