
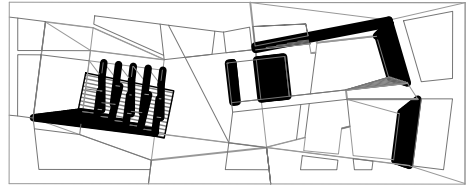



Millimetres

0 10 100

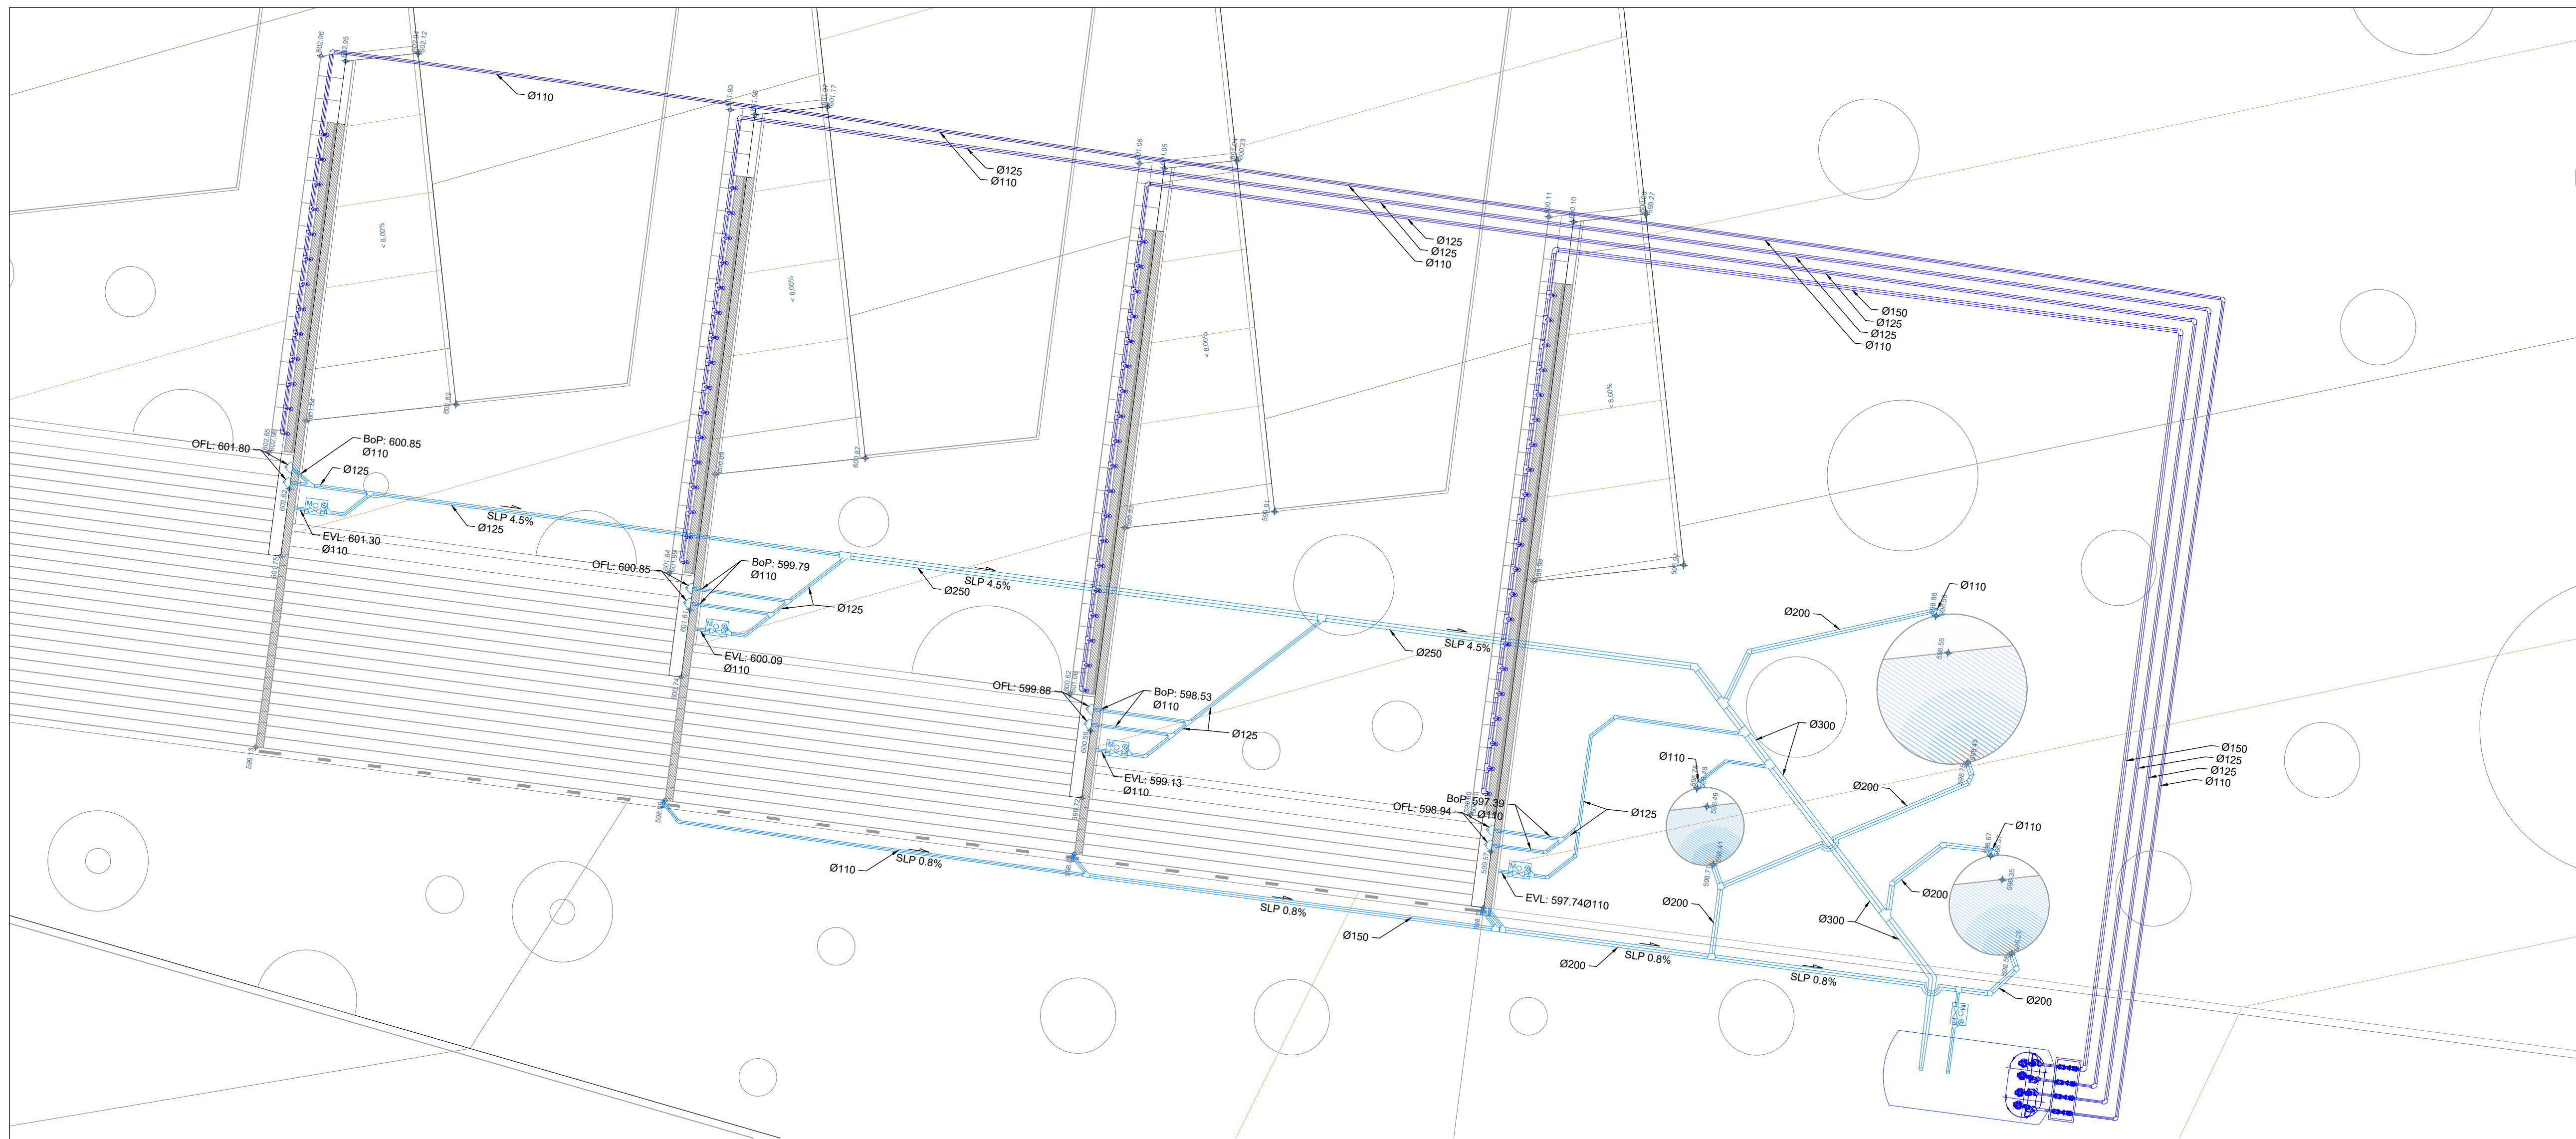

LEGEND

- SUPPLY NOZZLE (FROM THE BOTTOM)
- SUPPLY NOZZLE (FROM THE SIDE)
- VERTICAL SLOT FOR OVERFLOW
- FLOOR DRAIN TO EMPTY THE WATER FEATURE
- SUPPLY PIPE (PRESSURIZED)
- RETURN PIPE (BY GRAVITY)
- SHUT OFF VALVE IN MANHOLE
- MOTORIZED VALVE IN MANHOLE
- SUPPLY SUBMERSIBLE PUMP
- CLEAN OUT (TO CLEAN THE PIPEWORK)
- DRAIN GRATE

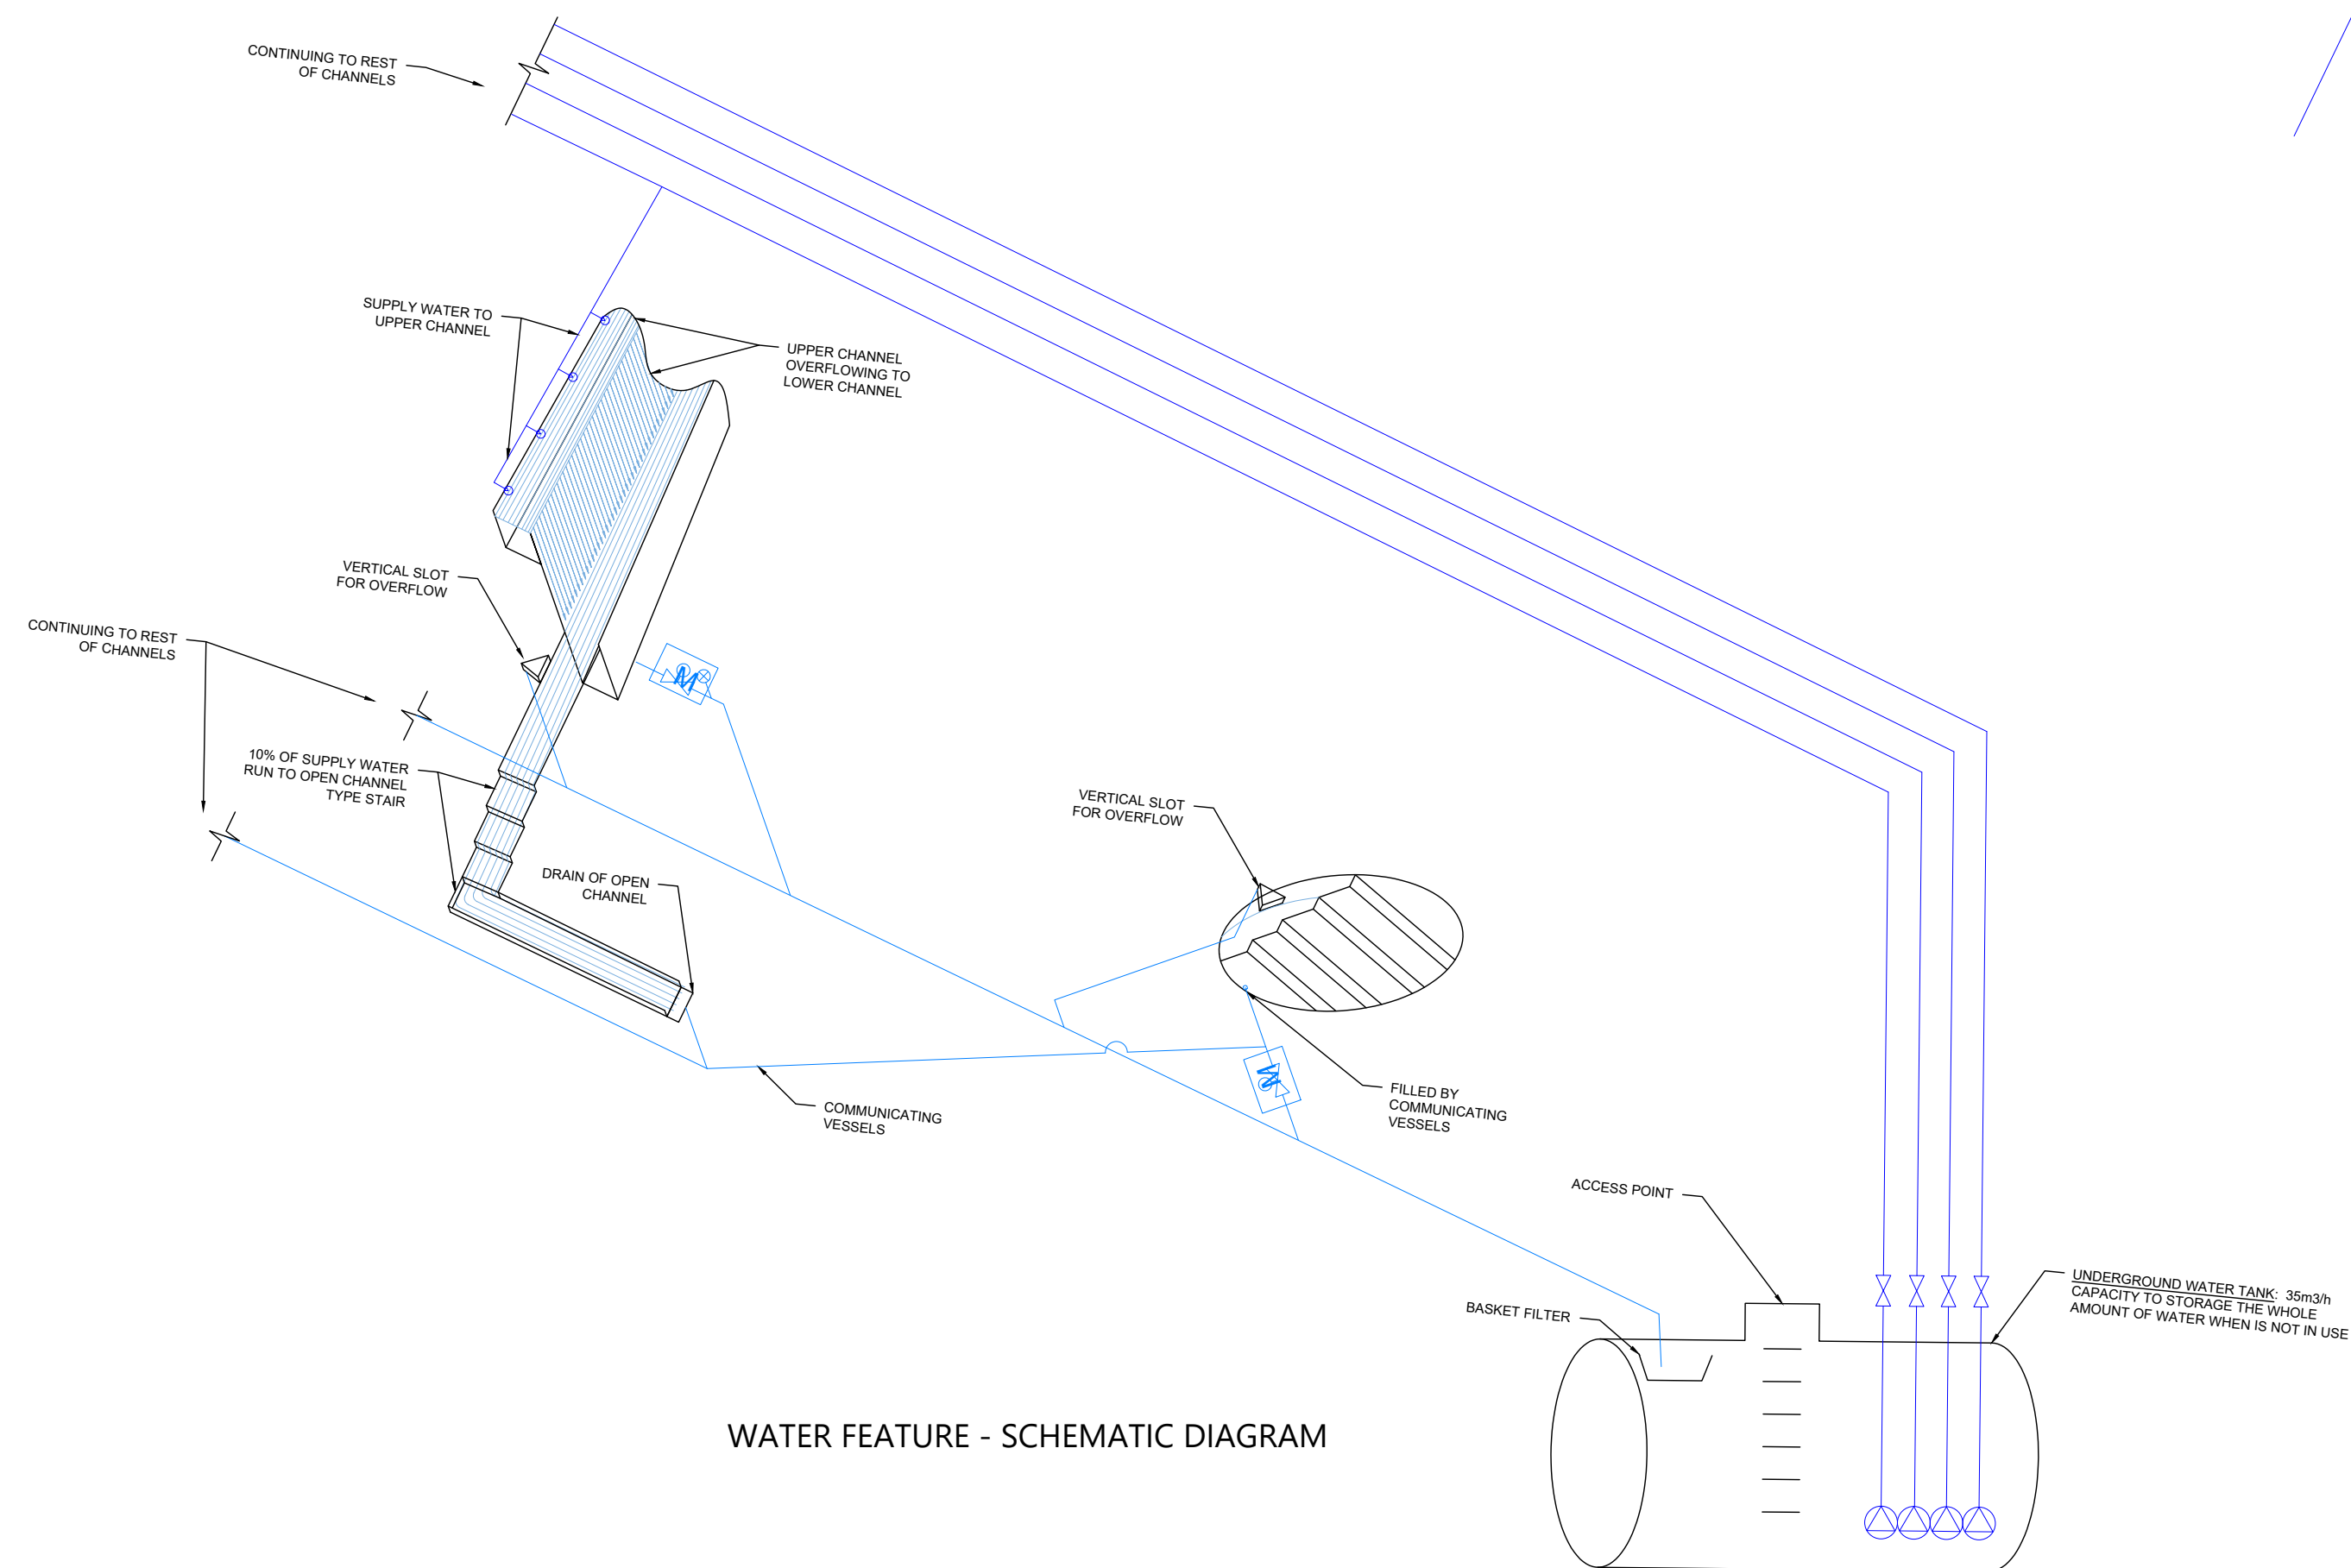

WATER FEATURE - SCHEMATIC DIAGRAM

AF	SEP 2023	DETAILED DESIGN	XXX	XXX	XXX
AE	JUL 2023	DETAILED DESIGN	XXX	XXX	XXX
AD	APR 2023	DETAILED DESIGN	XXX	XXX	XXX
AC	MAR 2023	DETAILED DESIGN	XXX	XXX	XXX
AB	FEB 2023	DETAILED DESIGN	XXX	XXX	XXX
AA	DEC 2022	DETAILED DESIGN	XXX	XXX	XXX
Rev.	Date	Description	By	Chk'd	App'd

CLIENT	DESIGNER

Project Title
LANDSCAPE DESIGN OF CITY PARKS, AR-RIMAL 2, AL-QADISIYAH 3, AL-MONASYA , TWAEEQ 2

Drawing Title
**AL-MONASYA
WATER FEATURE
HIDRONIC SYSTEM**

Scale 1:150	Designed XXX	Drawn XXX	Checked XXX	Approved XXX
Original Size A1	Date SEP 2023	Date SEP 2023	Date SEP 2023	Date SEP 2023
Drawing Number JVEA-GRP-MON-WTF-5105				Revision AF